AD.01	FACADEBEKLÆDNING "1 PÅ 2" 339 mm 27/15 mm "1 på 2" facadebeklædning som Kjellerup (L5 og L6) Farve: aftales nærmere Materialeklasse facadebeklædning: B-s2,d0 38x73 mm lægte vandret cc 600 mm 25x50 mm afstandsliste NTR-AB 9 mm vindspærreplade Swisspearl Extreme 45x195 mm regler fastgjort til betonelement iht. ingeniør 195 mm mineraluld kl. 34 45 mm mineraluld kl. 34
AD.02	FACADEBEKLÆDNING "1 PÅ 2" 333 mm 21/15 mm "1 på 2" facadebeklædning som Kjellerup (L1 og L2) Farve: aftales nærmere Materialeklasse facadebeklædning: B-s2,d0 38x73 mm lægte vandret cc 600 mm 25x50 mm afstandsliste NTR-AB 9 mm vindspærreplade Swisspearl Extreme 45x195 mm regler fastgjort til betonelement iht. ingeniør 195 mm mineraluld kl. 34 45 mm mineraluld kl. 34
AD.03	SKILLEVÆG LET Teleskopløsning mod betonhuldæk min. 30 mm Udføres efter leverandørens anvisning 2x12,5 mm Fibergips som Fermacelle 75 mm stålskelet som Fermacell stålsystem 70 mm stenuld min. 30 kg/m3 2x12,5 mm Fibergips som Fimrecelle Spartles og malerbehandles efter malerbehandlingsanvisning V2674 - Glans 10
AD.04	FORSATSVÆG VED INSTALLATIONER Teleskopløsning mod betonhuldæk min. 30 mm Udføres efter leverandørens anvisning 2x12,5 mm Fibergips 75 mm stålskelet som Fermacell stålsystem Spartles og malerbehandles efter malerbehandlingsanvisning V2674 - Glans 10
AD.05	SKILLEVÆG VED INDBYGNINGSCISTERNE Teleskopløsning mod betonhuldæk min. 30 mm Udføres efter leverandørens anvisning 2x12,5 mm Fibergips 75 mm stålskelet som Fermacell stålsystem 70 mm mineraluld 40 mm mellemrum mellem stålskelet 75 mm stålskelet som Fermacell stålsystem 2x12,5 mm Fibergips Spartles og malerbehandles efter malerbehandlingsanvisning V2674 - Glans 10
AF.01	PRÆFABRIKERET BETONTRAPPE Detailprojekteres af leverandør Materiale: Beton Stigning: ca. 177 mm Grund: 280 mm Trin med rundede hjørner Malerbehandlet trædeflade som epoxy gulv i bådhal Skridsikre trin med kontrastfarve Brandtætning mellem trappe og væg iht. brandstrategi
BD.01	BETONELEMENTVÆG 180 mm 180 mm Betonelementvæg Dimension iht. Ingeniør Spartles og malerbehandles efter malerbehandlingsanvisning V2612 eller V26202 - Glans 10
BD.02	BETONELEMENTVÆG 150 mm 150 mm Betonelementvæg Dimension iht. Ingeniør Spartles og malerbehandles efter malerbehandlingsanvisning V2612 eller V26202 - Glans 10
FQC.01	HÅNDLISTE Håndliste i teaktræ
FQD.02	PULLERT VED VED RAMPE Pullert udføres af stålrør dy 197,3 mm med påsvejst slutmuffe h= 120 cm forsynes med 2 stk. 5 cm reflekser Der støbes betonfundament for pullert, pullert monteres med komprimeret sand i udsparring i fundament Placeres 10 cm fra bygning, højde 70 cm over terræn
FQD.03	PÅKØRSELSSIKRING Påkørselssikring omkring fritstående søjler iht. ingeniør
NCB.01	VÆGKLINKER VÅDRUM Vægklinker efter aftale Fliseklæb Vådrumsmembransystem
NCB.02	BRANDINDDÆKNING AF STÅLRAMMEBEN Brandinddækning iht. Ingeniør Fra gulv og 2 meter op limes der 50x50x0,5 mm rustfri hjørnevinkler
NCH.01	INDDÆKNING PORTÅBNING Udvendig alu. Inddækning Farve: efter aftale Korrisionsklasse C5-2
QQC.01	DØR HOVEDINDGANG Hvidbjerg Everluxx Classic Opdeling se facade Farve: aftales nærmere U-værdi jf. gældende energiramme Dørlukker som: Dorma TS93 ADK med briklæser og kodetastatur Med karmoverførsel for ADK Elektronisk sikring: Sikringsklasse 30-S
QQC.03	PLADEDØR BÅDHAL FP Alu. Farve: aftales nærmere U-værdi jf. gældende energiramme Dørlukker som: Dorma TS93 ADK med briklæser og kodetastatur Med karmoverførsel for ADK Elektronisk sikring: Sikringsklasse 30-S
QQD.01	INSPEKTIONSLEM Dimension 500x500 mm Placeres 400 mm over færdigt gulv
QQE.01	LEDHEJSEPORT BÅDHAL Nassau 9000F Foam aluminium BxH: 7000x6000 mm U-værdi jf. gældende energiramme Farve: RAL 6005 Påmales eller folieres med krydsflag jf. udbud ADK med tastatur og briklæser Sikringsklasse 30-S
QQE.02	LEDHEJSEPORT GARAGEL Nassau 9000F Foam aluminium BxH: 5500x4000 mm U-værdi jf. gældende energiramme Farve: RAL 6005 ADK med tastatur og briklæser Sikringsklasse 30-S
RB.06	KEMISKAB Kemiskab til opbevaring af POL produkter HxBxD: 2000x1000x450 mm Udsugning iht. Ingeniør
RD.01	DISELTANK 2500 l dieseltank med udvendig påfyldningsstuds
UNC.02	BØJLESTANG HOVEDINDGANG Bøjlestang til overtøj Placeret indenfor ved indgangsdør
WPA.01	TAGNEDLØB Tagnedløb føres gennem klimaskærm, gennemføringet tætnes Der laves en rensemulighed på 1. etage Dimension og tilslutning iht. Ing.
XLH.01	LINJEAFLØB 1000 mm linjeafløb Type iht. Ingeniør
XLH.03	LINJEAFLØB 1300 mm linjeafløb Type iht. Ingeniør
XLH.04	LINJEAFLØB ACO - MODULAR 200 Fald i renden Dim. Iht Ingeniør

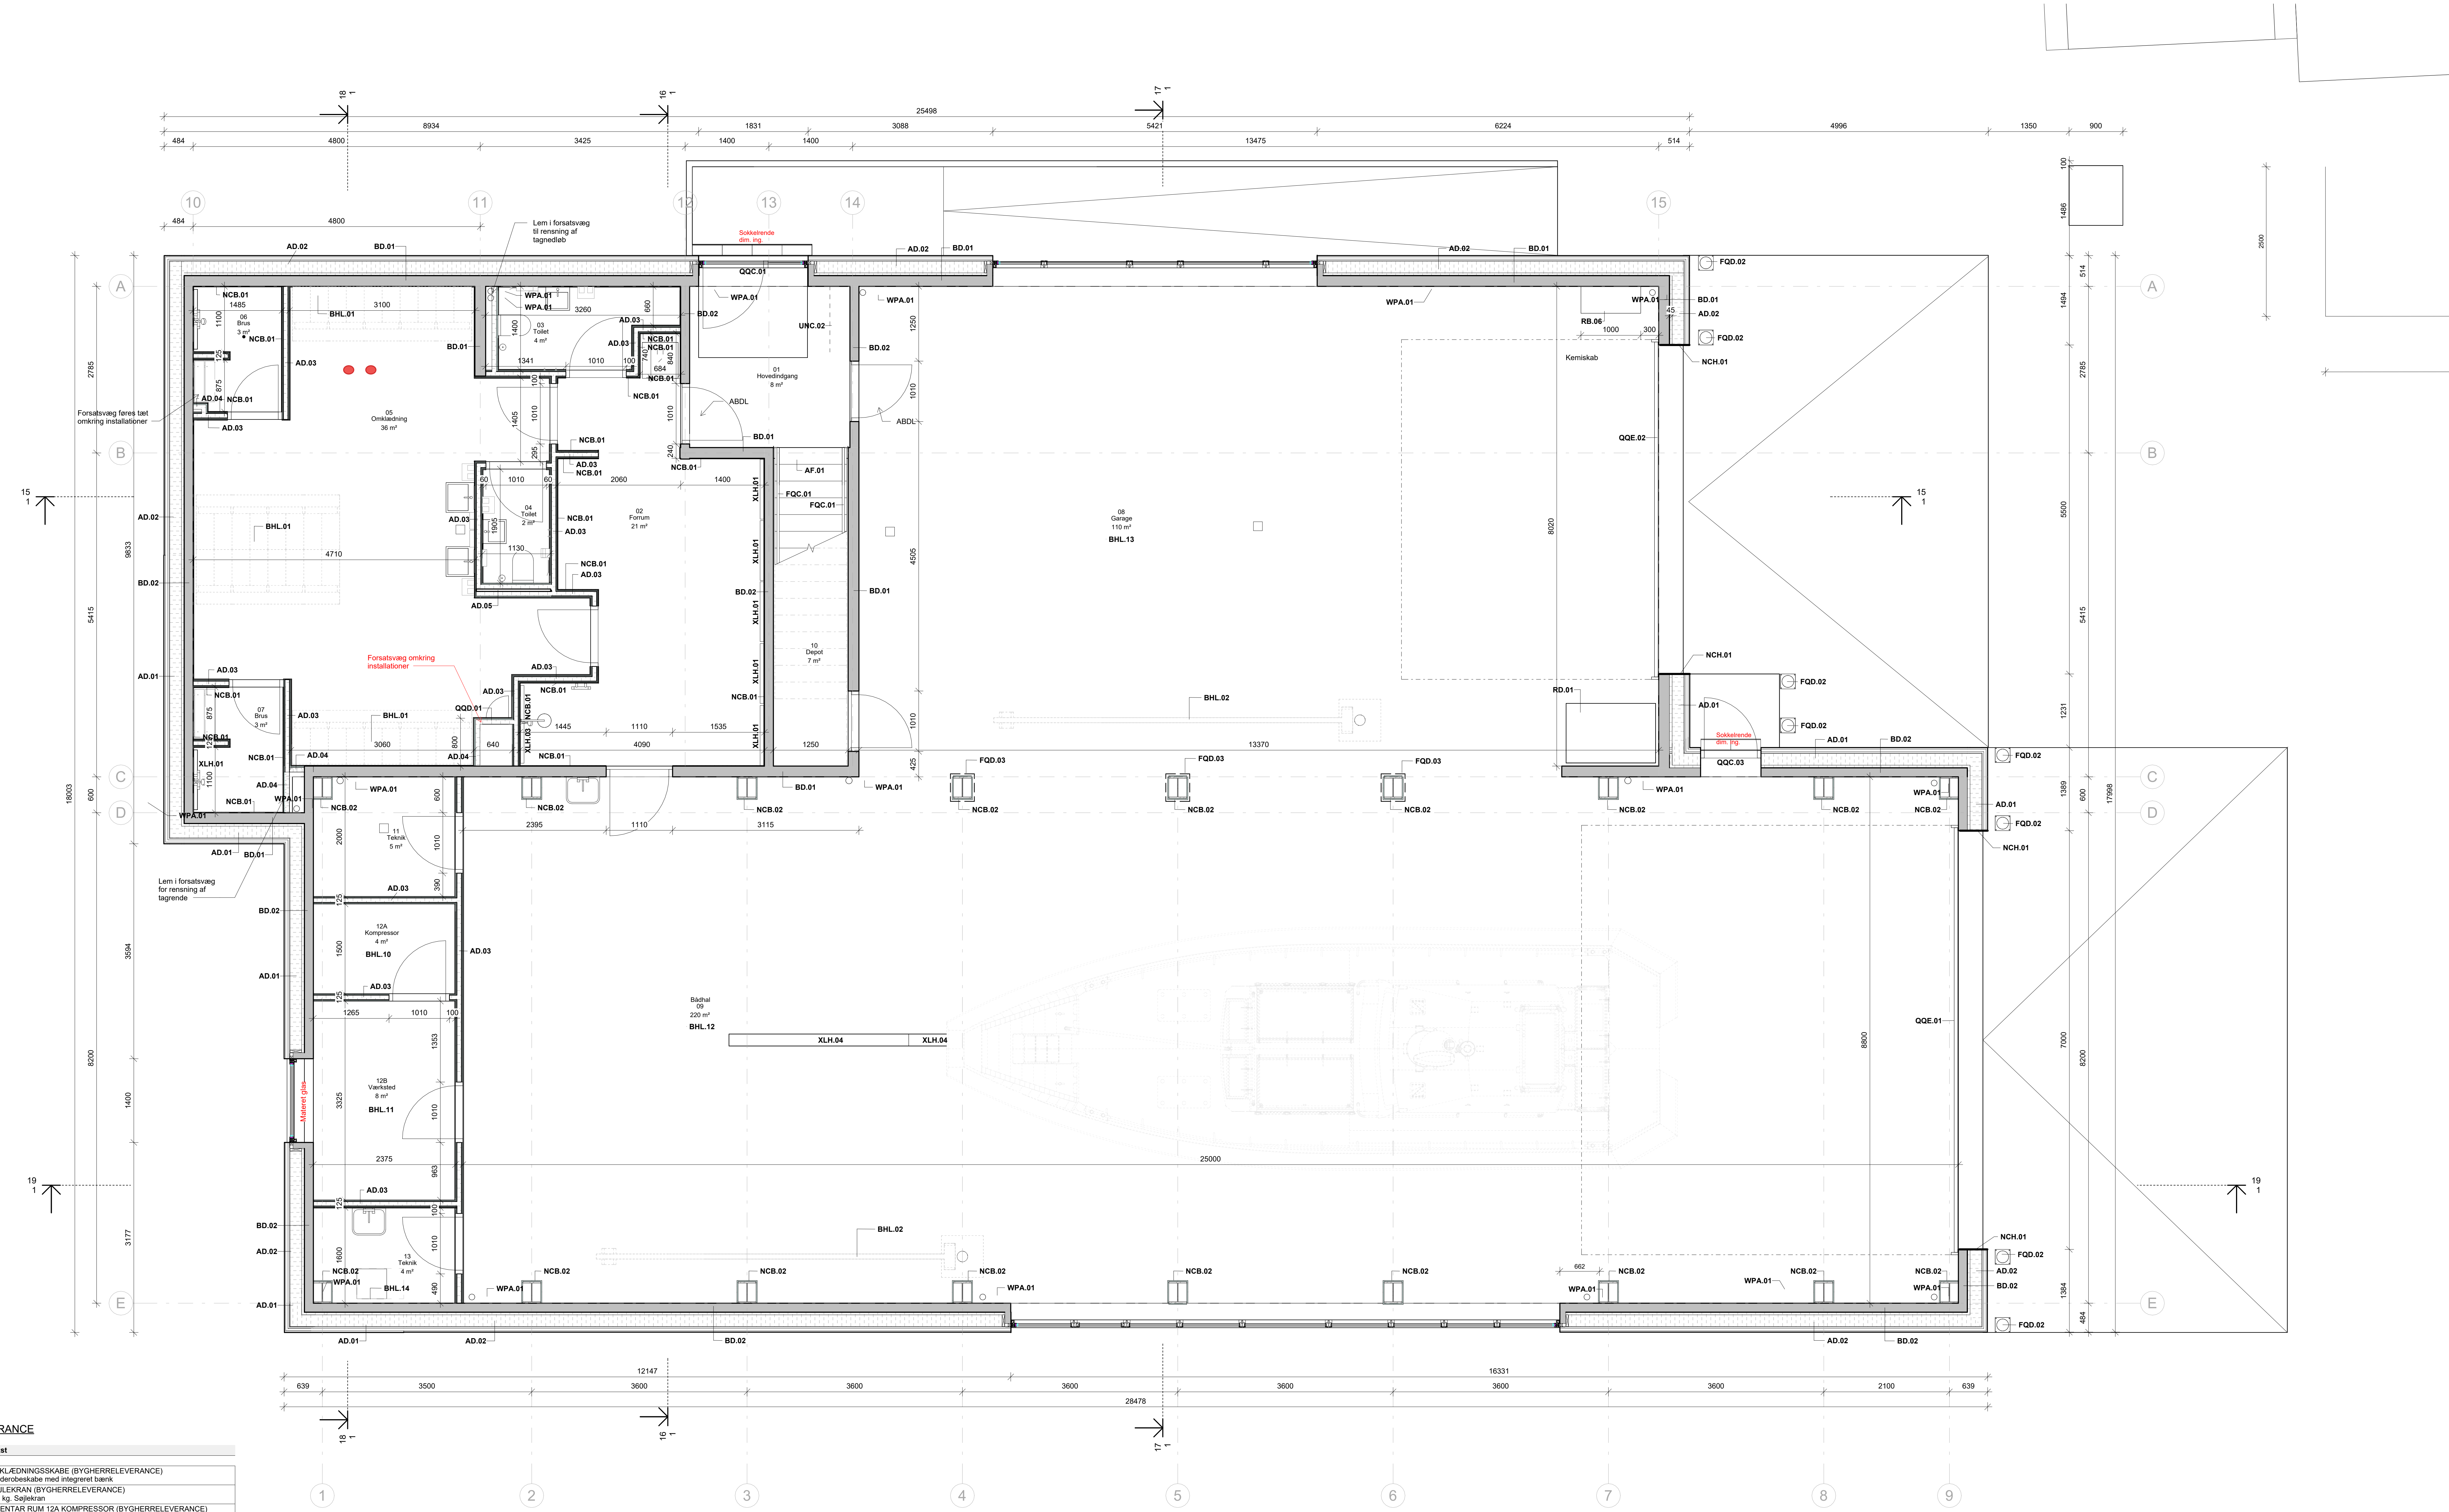

BYGHERRELEVERANCE

Identifikation	Tekst
BHL.01	OMKLÆDNINGSSKABE (BYGHERRELEVERANCE) Garderobeskabe med integreret bænk
BHL.02	SØJLEKRAN (BYGHERRELEVERANCE) 250 kg. Søjlekran
BHL.10	INVENTAR RUM 12A KOMPRESSOR (BYGHERRELEVERANCE) Trykluftkompressor
BHL.11	INVENTAR RUM 12B VÆRKSTED (BYGHERRELEVERANCE) Opbevaringsskabe, filebænk, værktøjsophængstavle og svejseanlæg
BHL.12	INVENTAR RUM 09 BÅDHAL (BYGHERRELEVERANCE) Filebænk, værktøjsophængstavle og opbevaringsskabe
BHL.13	INVENTAR RUM 08 GARAGE (BYGHERRELEVERANCE) Hedtvandsrenser og svejseanlæg
BHL.14	GULVVASKEMASKINE (BYGHERRELEVERANCE) Placering af installationer for gulvvaskemaskine

6120 REDNINGSSTATION NØRRE VORUPØR BYGNING 3 3 C-000628

Rev	Dato	Rettelser	Kontrol	Godkendt

FORSVARET

ETABLISSEMENT- OG TERRÆNKOMMANDOEN
Arsenalvej 55 DK-9800 Hjørring Tlf.: 728 13000 E-mail: fes@mil.dk

ETABNAVN
Bygnings-/Anlægsnavn
1. ETAGE

6120 REDNINGSSTATION NØRRE VORUPØR BYGNING 3
Etab. nr.: 6120
Bygn.-/Anlægsnr.: 3

Foreløbigt tryk
11-12-2025 15:50:27

Projektforslag ETK 3

Tegnet: TGN Kontrol: EMW Godk.: EMW Mål: 1 : 50 Dato: 28-11-2025 Klassifikation: IKL
Modelfiler: 6120-3-A
Tegningsfil: 6120-3-3
Produktionsplannr.: C-000628

● HMC Byg og Anlæg A/S	Himmerlandsvej 16	9670 Løgstør	+45 9666 8800	Sag:	
○ P+P Arkitekter	Havnetorv 3, 1. TV	7700 Thisted	+45 9791 1990	Sag:	1832.25
○ Brix & Kamp A/S	Boeck-Hansens Vej 3	9000 Aalborg	+45 9812 7866	Sag:	7949
○				Sag:	